PŮDORYS 1. NP

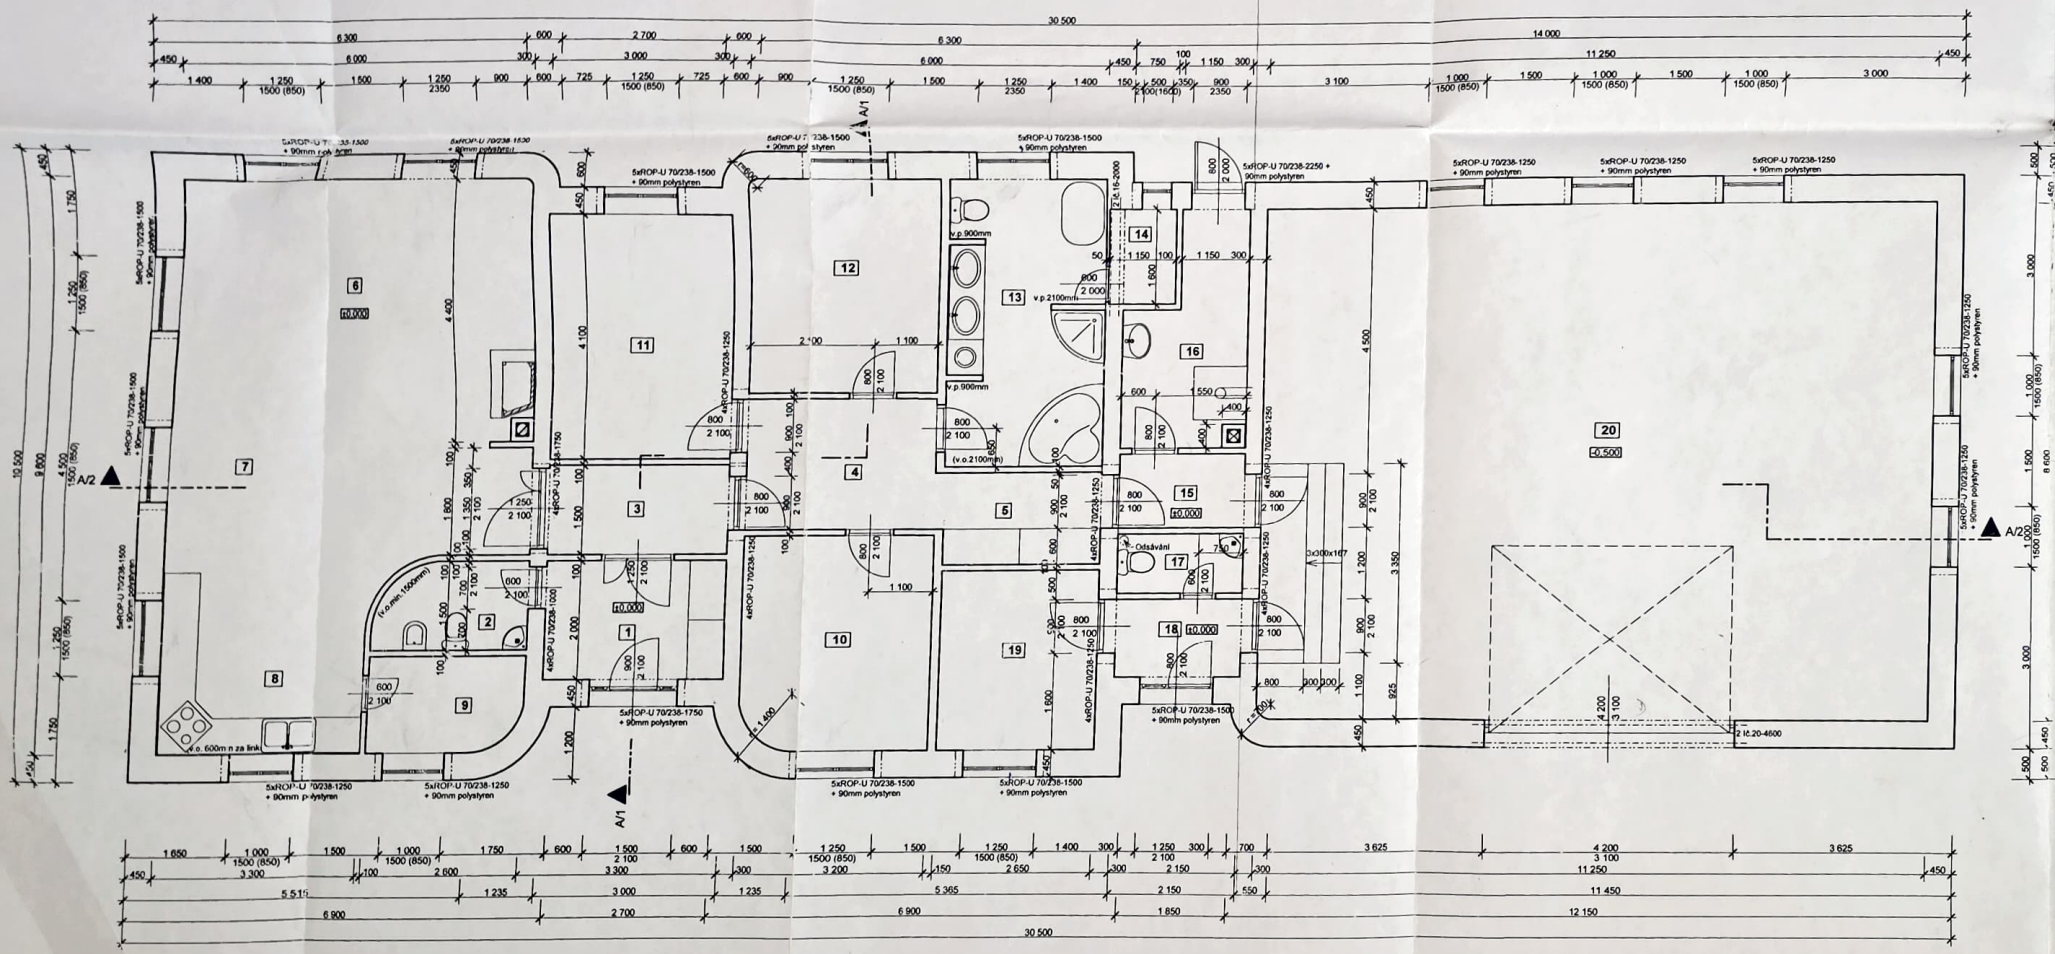
30 500
14 000
11 250
6 300
6 000
2 700
3 000
1 400
1 250
1500 (850)
1 500
1 250
2350
900
600
725
1 250
1500 (850)
725
600
900
1 250
1500 (850)
1 500
1 250
2350
1 400
150
500
350
900
2350
3 100
1 000
1500 (850)
1 500
1 000
1500 (850)
1 500
1 000
1500 (850)
3 000
A/1
A/2
5xROP-U 70/238-1500
+ 90mm polystyren
5xROP-U 70/238-1250
+ 90mm polystyren
5xROP-U 70/238-1750
+ 90mm polystyren
5xROP-U 70/238-2250 +
90mm polystyren
4xROP-U 70/238-1250
4xROP-U 70/238-1500
4xROP-U 70/238-1750
v.p.900mm
v.p.2100mm
(v.o.2100mm)
(v.o.min.1500mm)
v.o. 600mm za linkou
Odsávání
3x300x167
2 lz.20-4600
±0,000
-0,500
6
7
8
9
1
2
3
4
5
10
11
12
13
14
15
16
17
18
19
20
10 500
9 800
4 500
1 750
1 250
1500 (850)
4 400
4 100
2 100
1 100
800
2 100
1 250
2 100
600
2 100
1 350
350
1 800
100
1 500
2 000
1 200
450
1 600
530
2 100
900
2 100
1 100
800
2 100
1 550
400
1 150
300
1 800
50
2 000
4 500
3 350
925
4 200
3 100
1 650
1 000
1500 (850)
1 500
1 000
1500 (850)
1 750
600
1 500
2 100
600
1 500
1 250
1500 (850)
1 500
1 250
1500 (850)
1 400
300
1 250
2 100
300
700
3 625
4 200
3 100
3 625
450
3 300
100
2 600
3 300
300
150
2 650
300
2 150
300
11 250
450
5 515
1 235
3 000
1 235
5 365
2 150
550
11 450
6 900
2 700
6 900
1 850
12 150
30 500

VÝPIS MÍSTNOSTÍ Přízemí

OZNAČENÍ	ÚČEL MÍSTNOSTI	PLOCHA V m2	PODLAHOVÁ KRYTINA
1	Zádveří	6,00	Keramická dlažba
2	WC	3,60	Keramická dlažba
3	Chodba	4,61	Keramická dlažba
4	Hala	7,04	Keramická dlažba
5	Šatna	4,13	Keramická dlažba
6	Obývací pokoj	26,21	Dřevěná plovoucí
7	Jídelna	11,32	Dřevěná plovoucí
8	Kuchyň	8,42	Keramická dlažba
9	Spíž	3,98	Keramická dlažba
10	Ložnice	11,34	Dřevěná plovoucí
11	Ložnice	12,30	Dřevěná plovoucí
12	Ložnice	11,52	Dřevěná plovoucí
13	Koupelna	12,99	Keramická dlažba
14	Sauna	1,84	Dřevěná palubka
15	Chodba	2,87	Keramická dlažba
16	Kotelna	7,08	Keramická dlažba
17	WC	2,15	Keramická dlažba
18	Zádveří	3,16	Keramická dlažba
19	Pracovna	7,95	Keramická dlažba
20	Garáž	97,24	Keramická dlažba

Celková plocha : 245,74 m2

10 500

5

Zodpovědný projektant	Vypracoval :	PROJEKCE
Ing. D. Hanzelková	Ing. D. Hanzelková	Ing.Dagmar Hanzelková
Kraj : Olomoucký	M.Ú. : Mohelnice	Nám.Tyrše a Fügnera 3 789 85 Mohelnice tel. 583 430 667, 602 573 747 E-mail: projekce.hanzelkova@cbox.cz
Investor : Pavel a Soňa Pařízkovi, A.Kašpara 10, Mohelnice		
Akce : Rodinný dům k.ú. Zavadilka, parcela č. 37	Datum :	Prosinec 2002
	Měřítko :	1:50
	Formát :	A 4
Stavební část : PUDORYS 1.NP	Číslo výkresu :	101.03

Projekt byl zpracován SW ArchiCAD - nejmodernější technologie, nejjednodušší ovládání